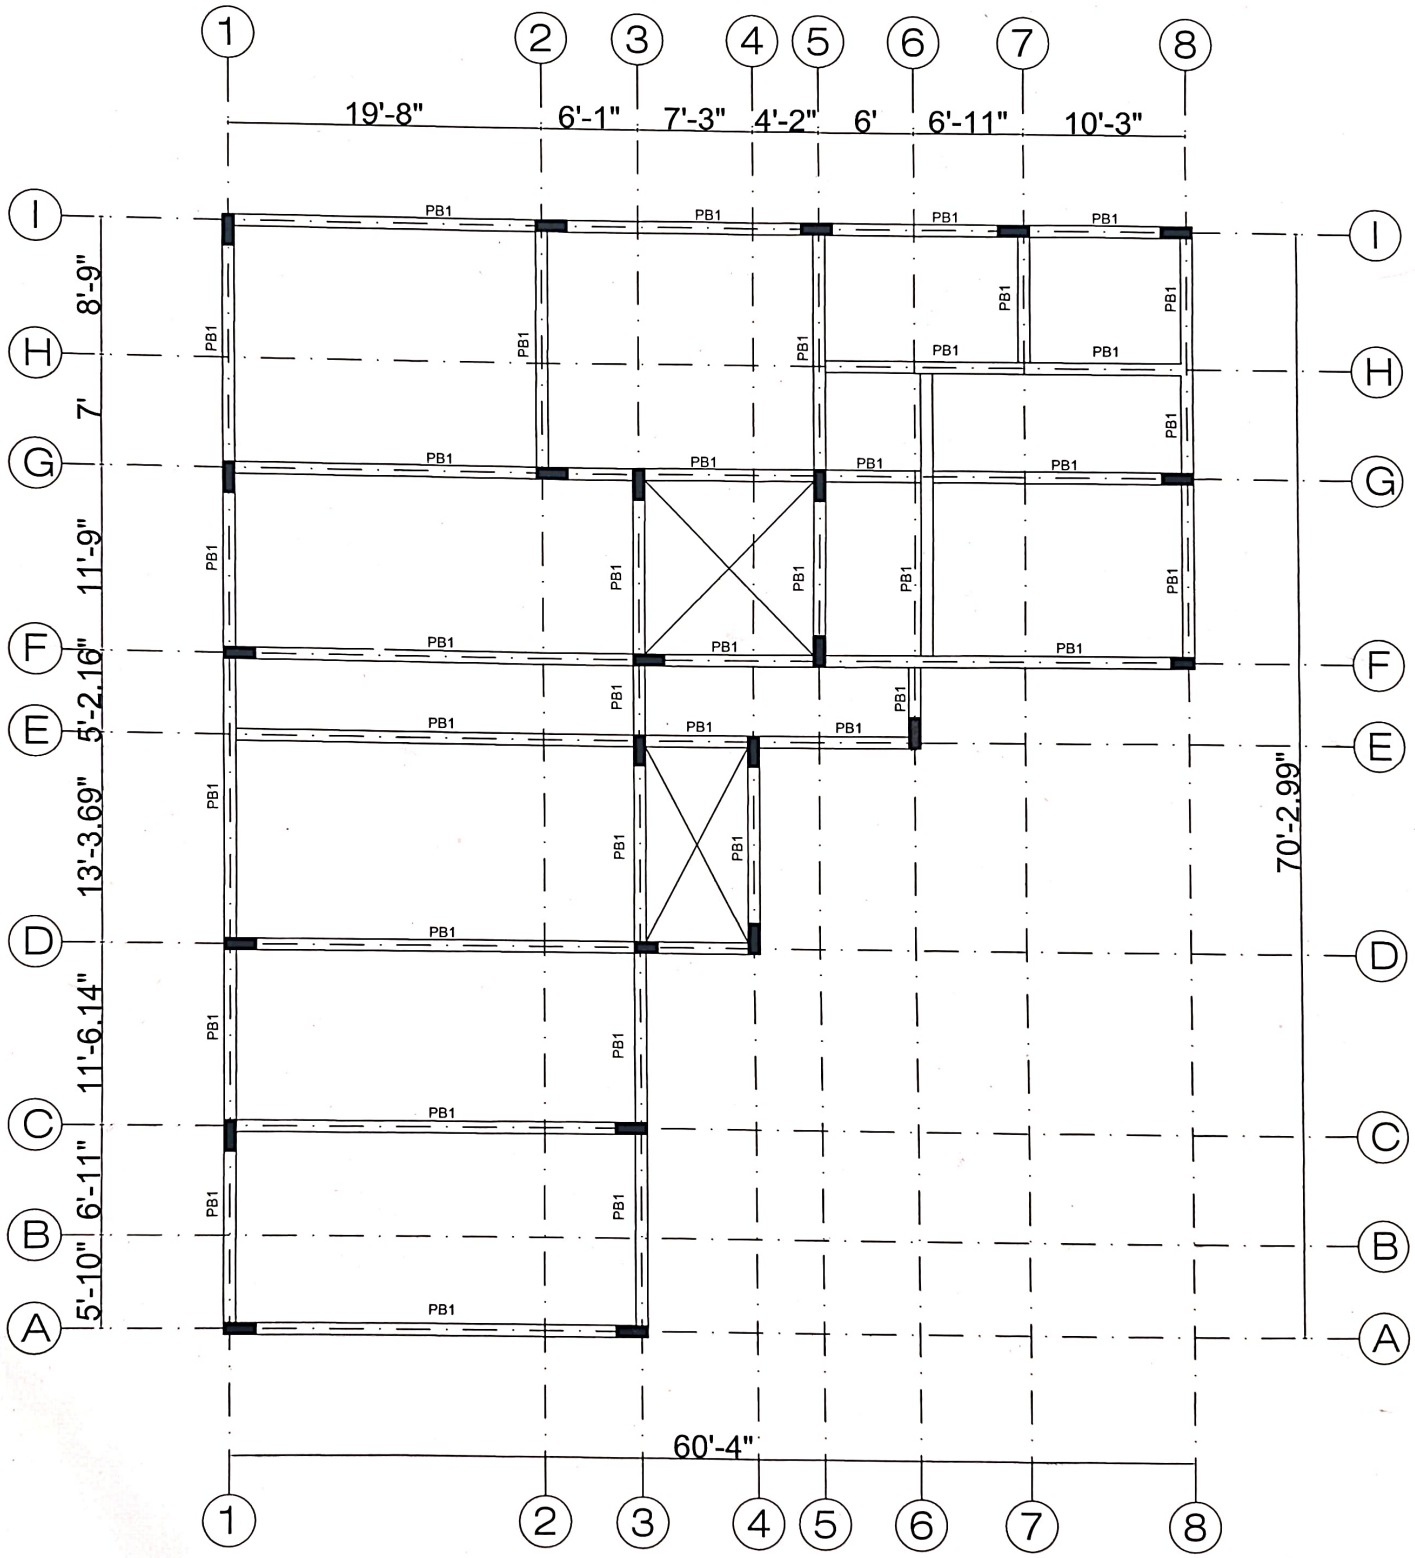

SCHEDULE OF PLINTH BEAM		
TYPE	SECTION	TYPICAL SECTION
PB1	9"X1'6"	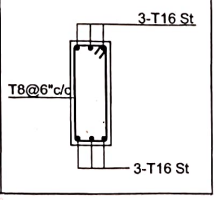

PLINTH BEAM REINFORCEMENT DETAILS