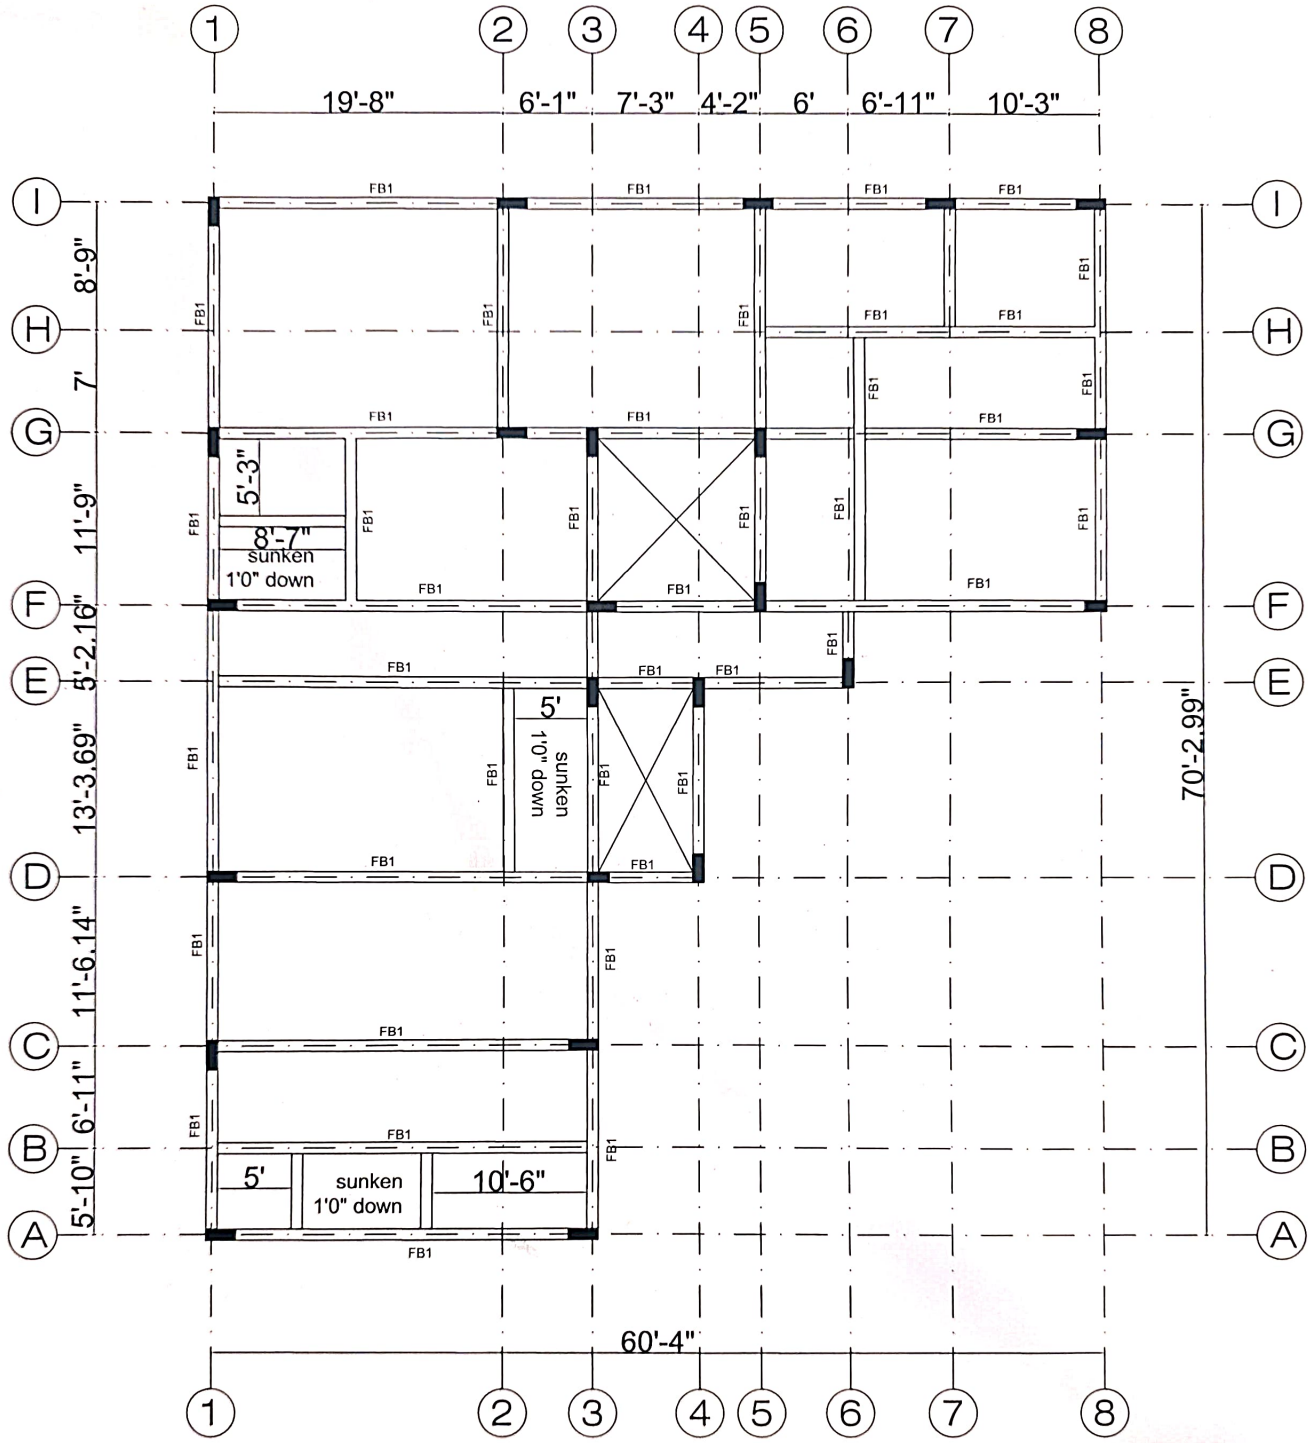

SCHEDULE OF FLOOR BEAM		
TYPE	SECTION	TYPICAL SECTION
FB1	9"X2'0"	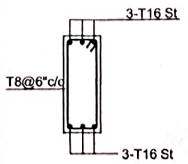

FLOOR BEAM REINFORCEMENT DETAILS