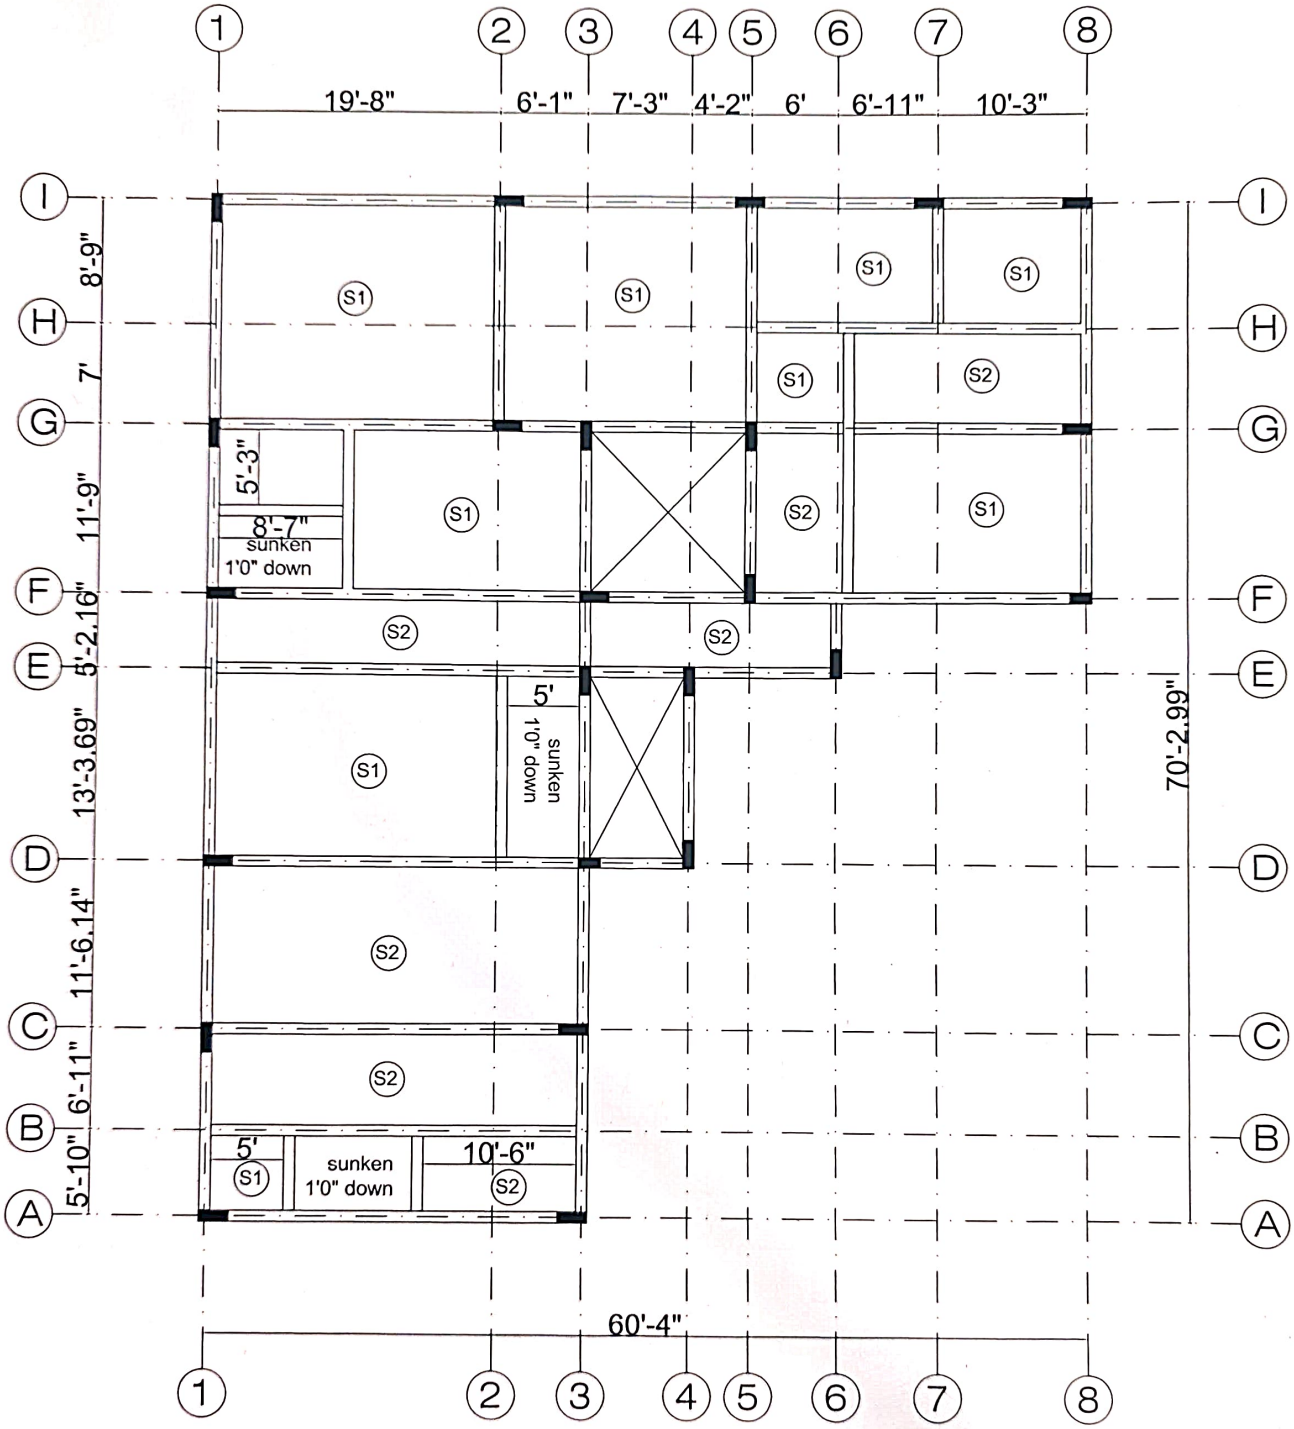

SLAB REINFORCEMENT DETAILS

SCHEDULE OF SLABS						
NOTATION	THICK.	TYPE	ALONG SHORTER SPAN		ALONG LONGER SPAN	
			MAIN REINF.	EXTRA. REINF.	DIST. REINF.	EXTRA. REINF.
S1	6"	↔	T10-6"c/c	T10-12"c/c	T8-6"c/c	T8-12"c/c
S2	6"	↕	T10-6"c/c	T10-12"c/c	T8-6"c/c	-