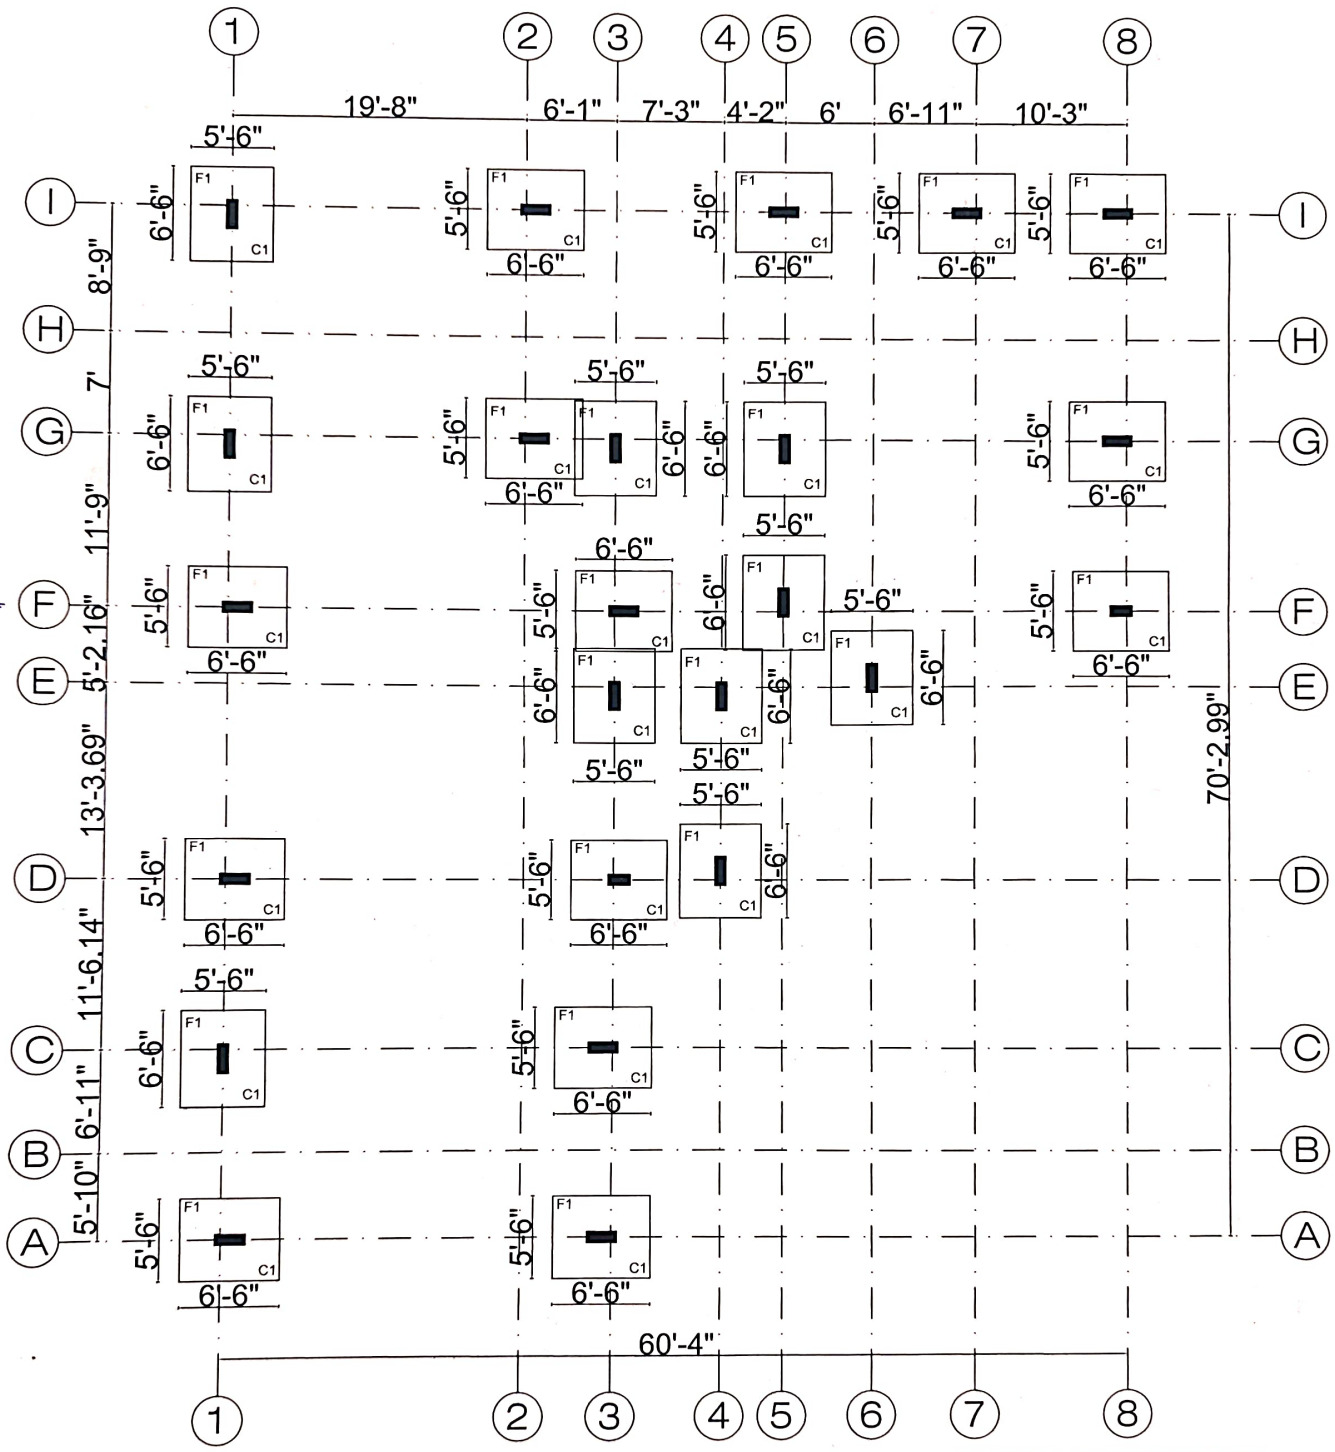

SCHEDULE OF FOOTINGS FOR SBC 95kN/m2								
SL.No.	TYPE	Nos.	EXCAVATION SIZE (LxB)	FOOTING SIZE		FOOTING DEPTH	BOTTOM REINF.	
				L	B	D	PARALLEL TO LENGTH	PARALLEL TO BREADTH
1	F1	24	6'-6"x7'-6"	5'-6"	6'-6"	18"	T12-6" c/c	T12-6" c/c

SCHEDULE OF COLUMN(Car porch)		
TYPE	SECTION	TYPICAL SECTION
C	9"X2'0"	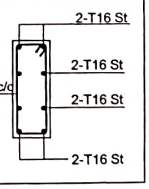

FOOTING & COLUMN REINFORCEMENT DETAILS

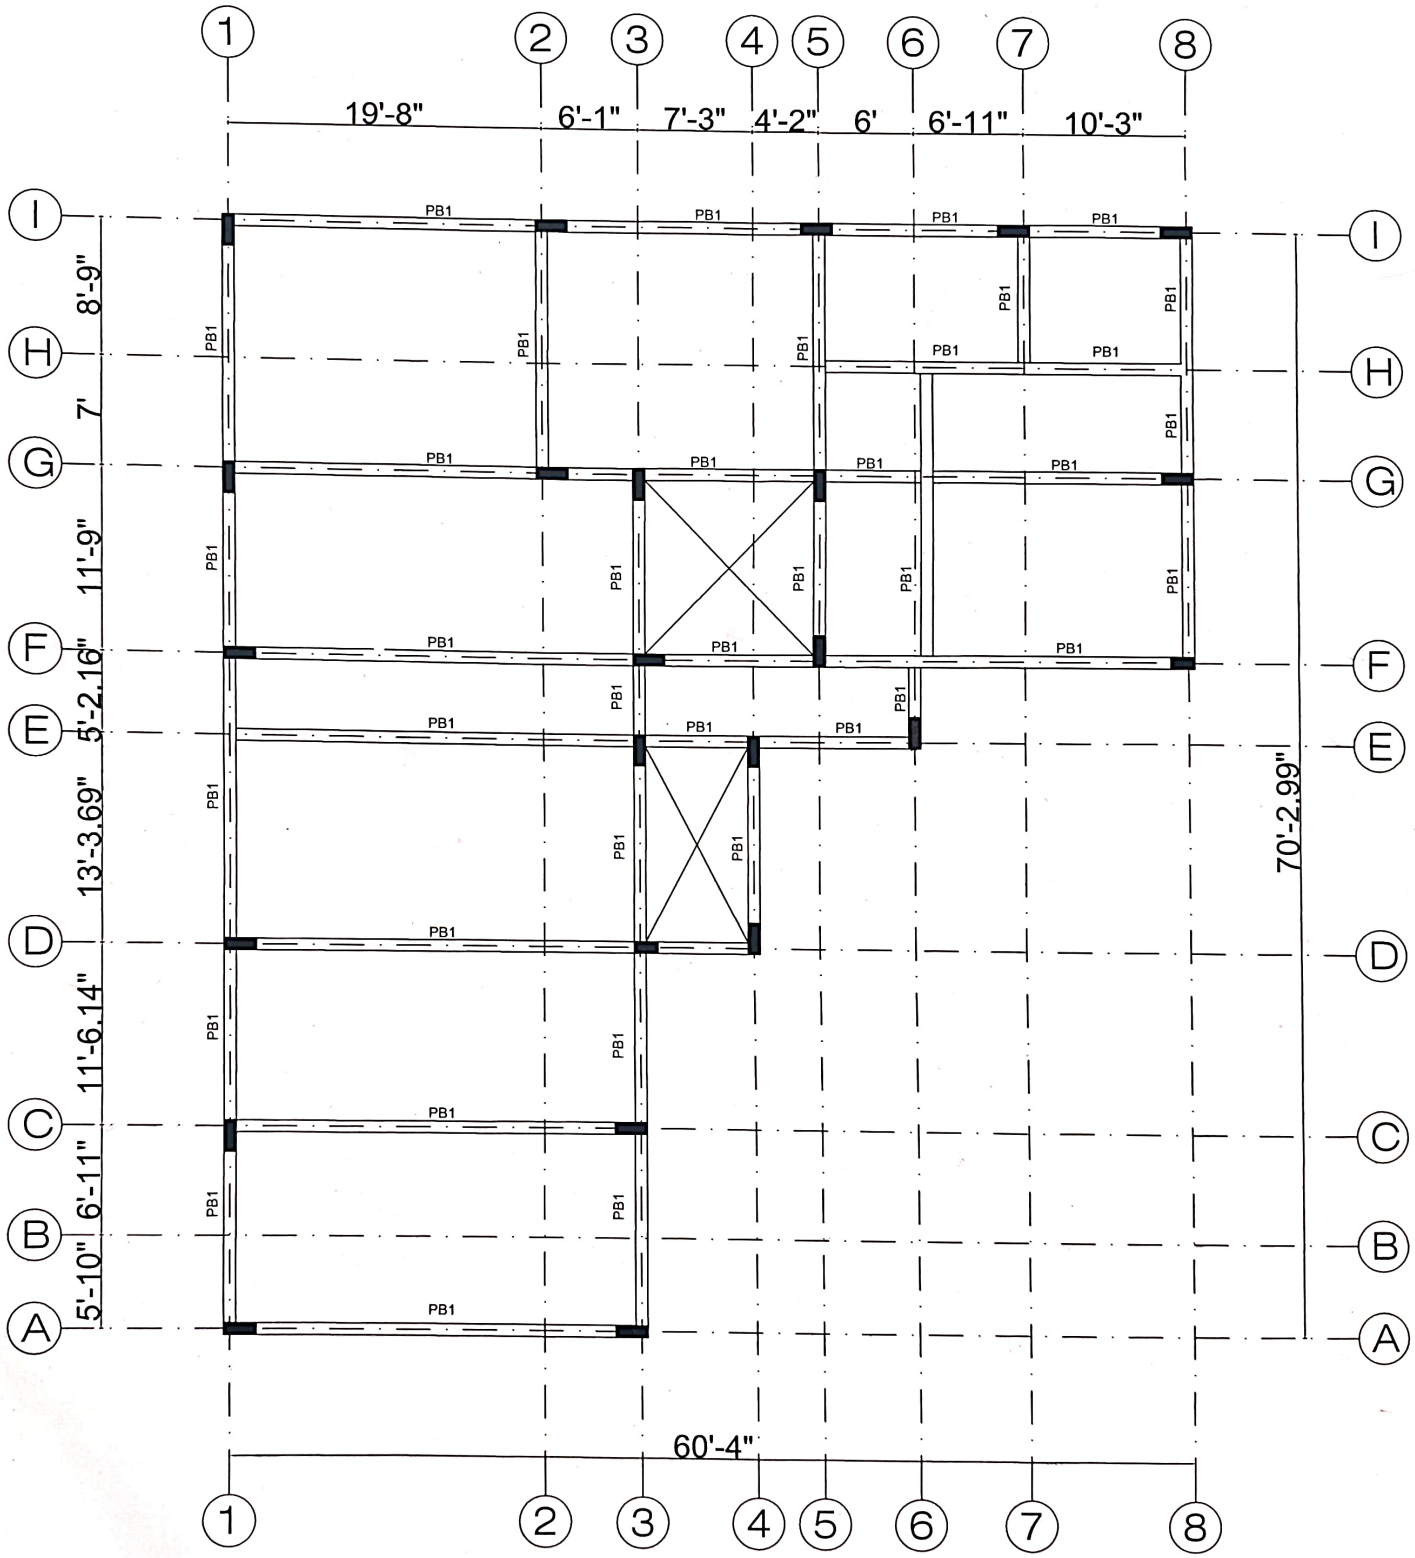

SCHEDULE OF PLINTH BEAM		
TYPE	SECTION	TYPICAL SECTION
PB1	9"X1'6"	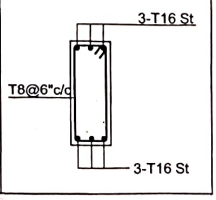

PLINTH BEAM REINFORCEMENT DETAILS

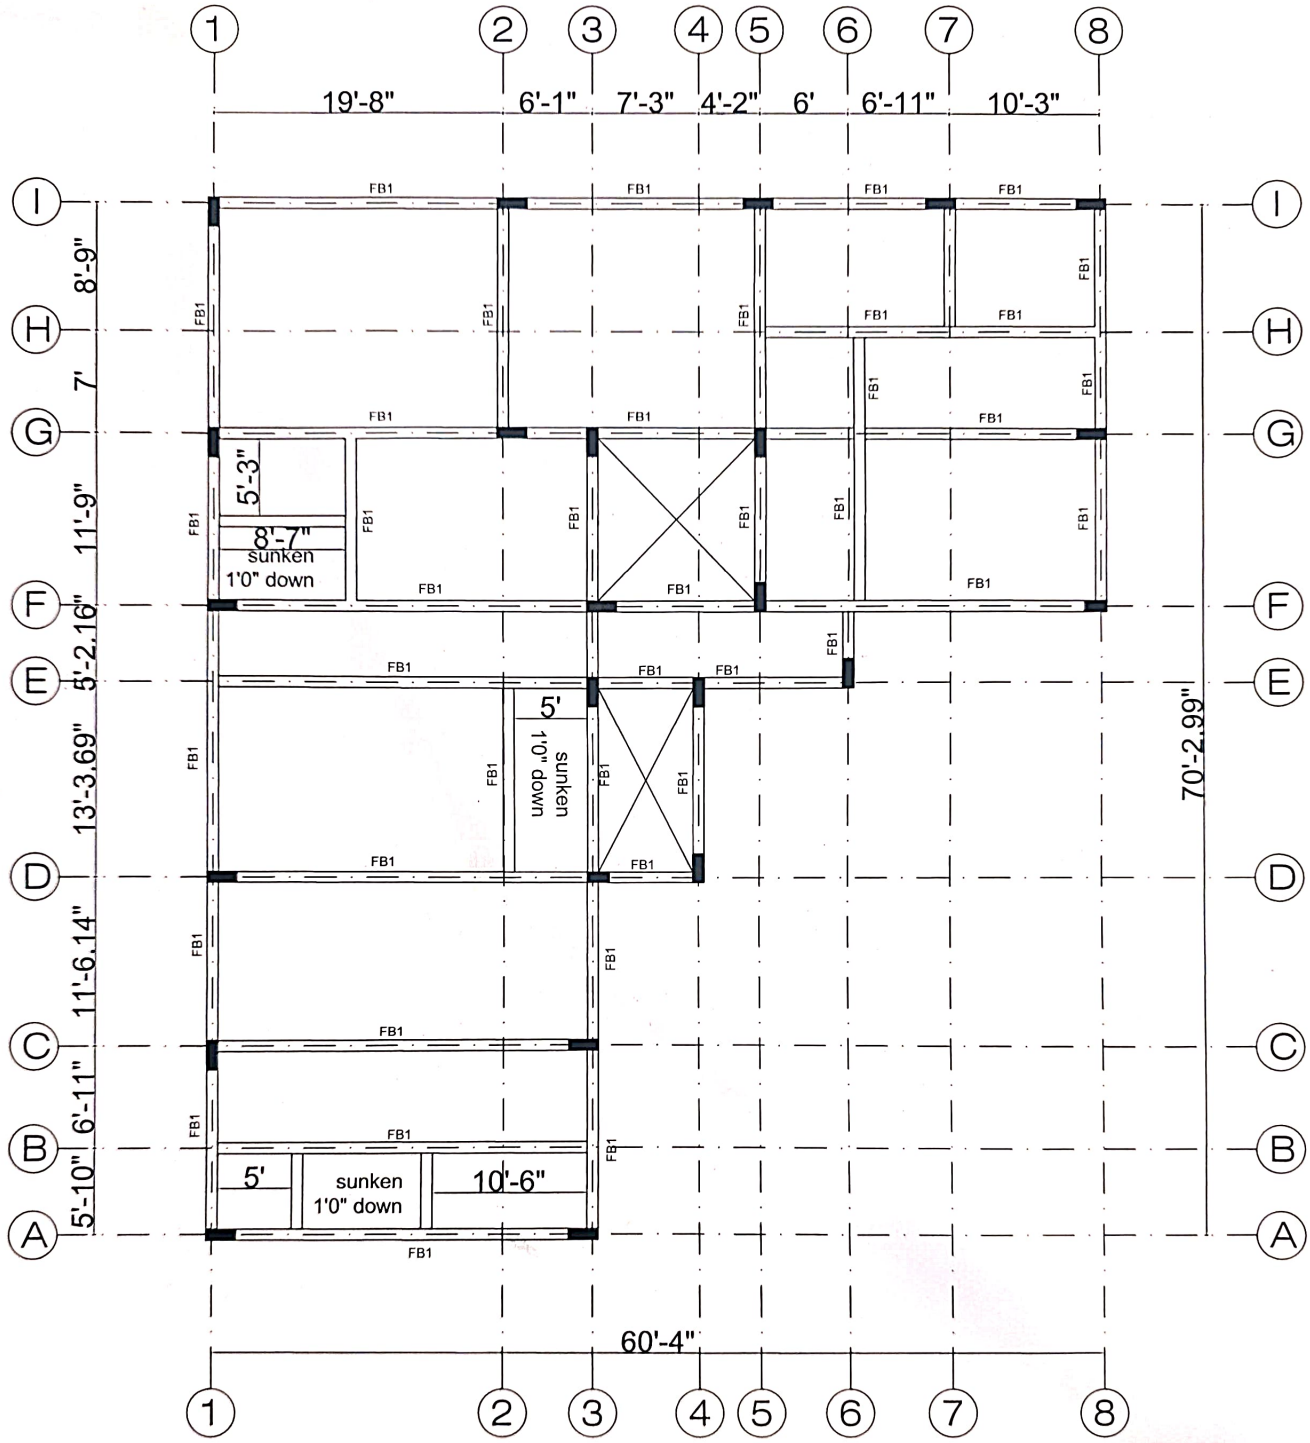

SCHEDULE OF FLOOR BEAM		
TYPE	SECTION	TYPICAL SECTION
FB1	9"X2'0"	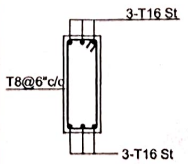

FLOOR BEAM REINFORCEMENT DETAILS

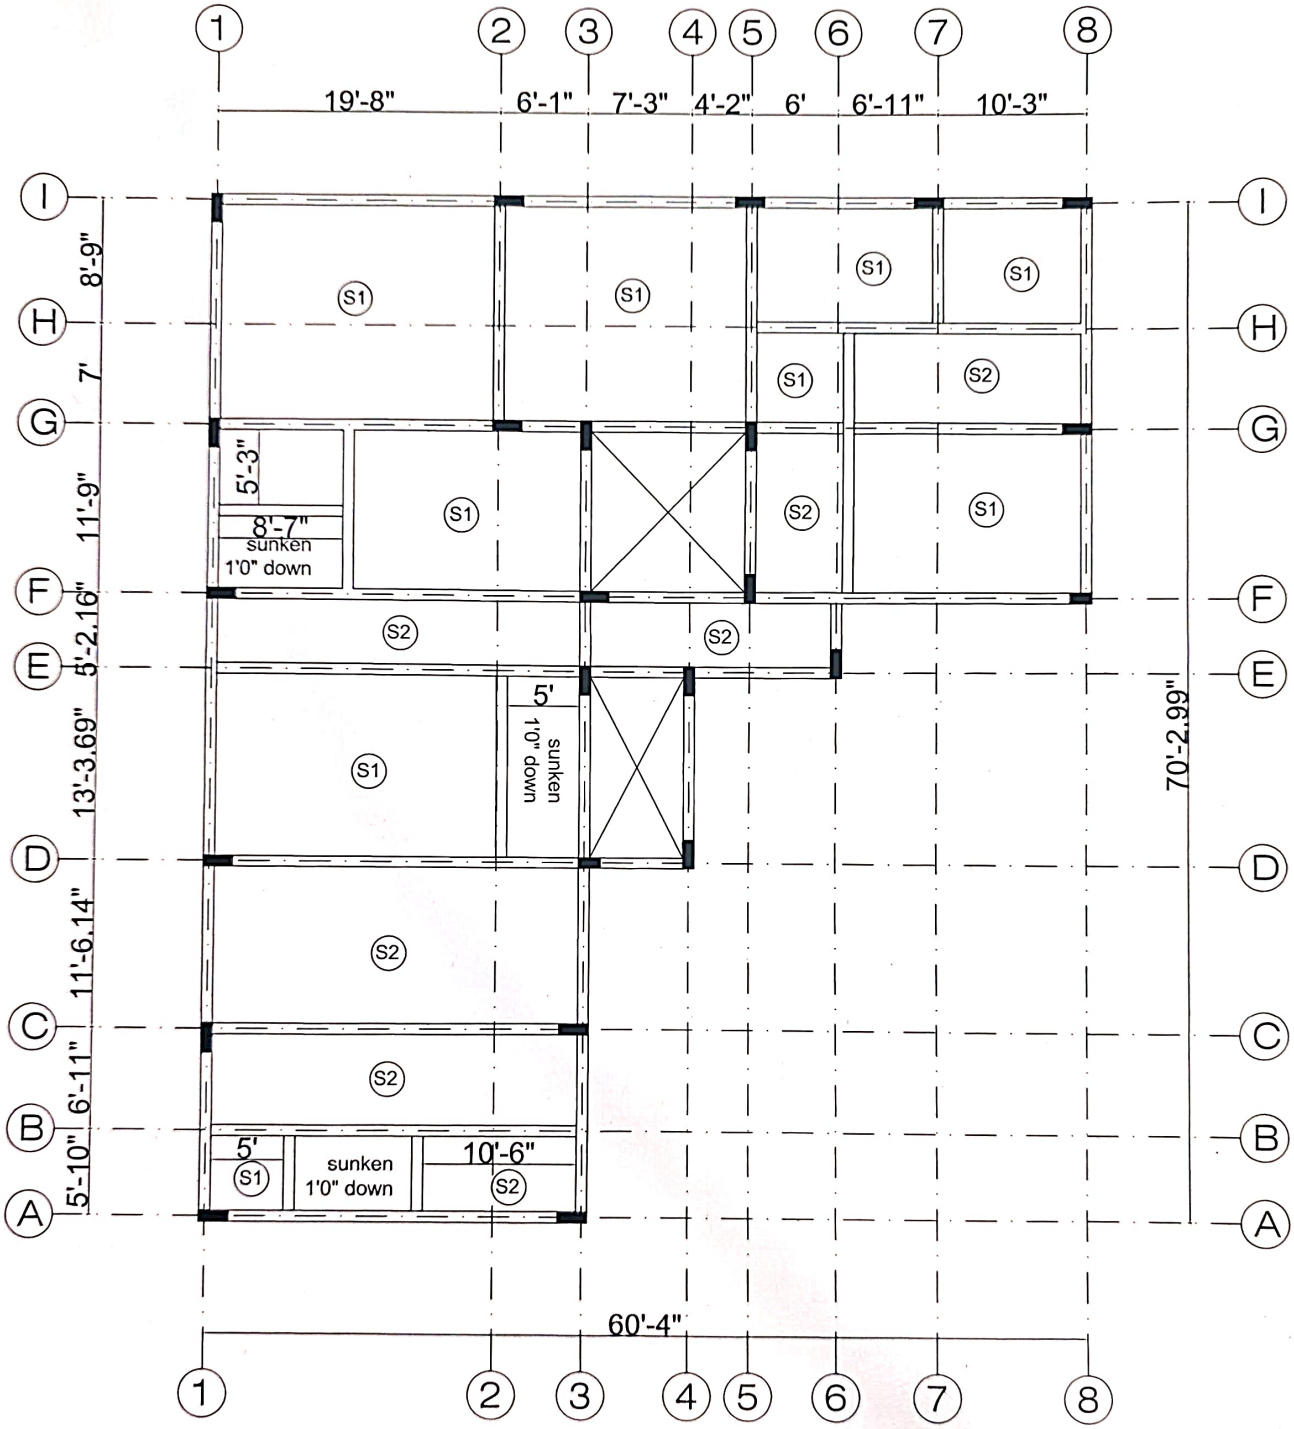

SLAB REINFORCEMENT DETAILS

SCHEDULE OF SLABS						
NOTATION	THICK.	TYPE	ALONG SHORTER SPAN		ALONG LONGER SPAN	
			MAIN REINF.	EXTRA. REINF.	DIST. REINF.	EXTRA. REINF.
S1	6"	↔	T10-6"c/c	T10-12"c/c	T8-6"c/c	T8-12"c/c
S2	6"	↕	T10-6"c/c	T10-12"c/c	T8-6"c/c	-